


Projectgegevens: Vercruysse Wouter

Keuringsformulier voor de elektrische installatie

Klant		Project omschrijving	
Naam	Vercruysse Wouter	Projectnaam	Vercruysse Wouter
Adres 1	Lendeleedsestraat 58	Projectbeschrijving	
Adres 2		Voeding	1x230V+N
Postcode	8870	Net	TT
Plaats	Izegem	EAN-Code	541449651000055687
Telefoon	+32497283279	Aardingsweerstand	... kΩ
		Isolatiweerstand	
E-mail	wouter.vercruysse@zure.com	Inspectie door:	
Aanmaakdatum	25/02/2025		
Gemaakt door	BD		
Installateur		Werkadres	
Naam	Suntronics Solar BV	Adres	
Adres 1	Toor 4	Postcode / Plaats	
Postcode / Plaats	8880 Ledegem	Telefoon	
Telefoon	+32 (0)56 49 89 80	Social Media	
E-mail	info@suntronics.be		
Ondernemingsnummer	BE 0568.568.369		
Afgevaardigde erkend organisme		Verantwoordelijke voor de uitvoering	
Naam		Naam	Suntronics Solar BV
	Handtekening		Handtekening
Datum	.. / .. / 20	Datum	23 / 04 / 2025

1 2 3 4 5 6 7 8 9

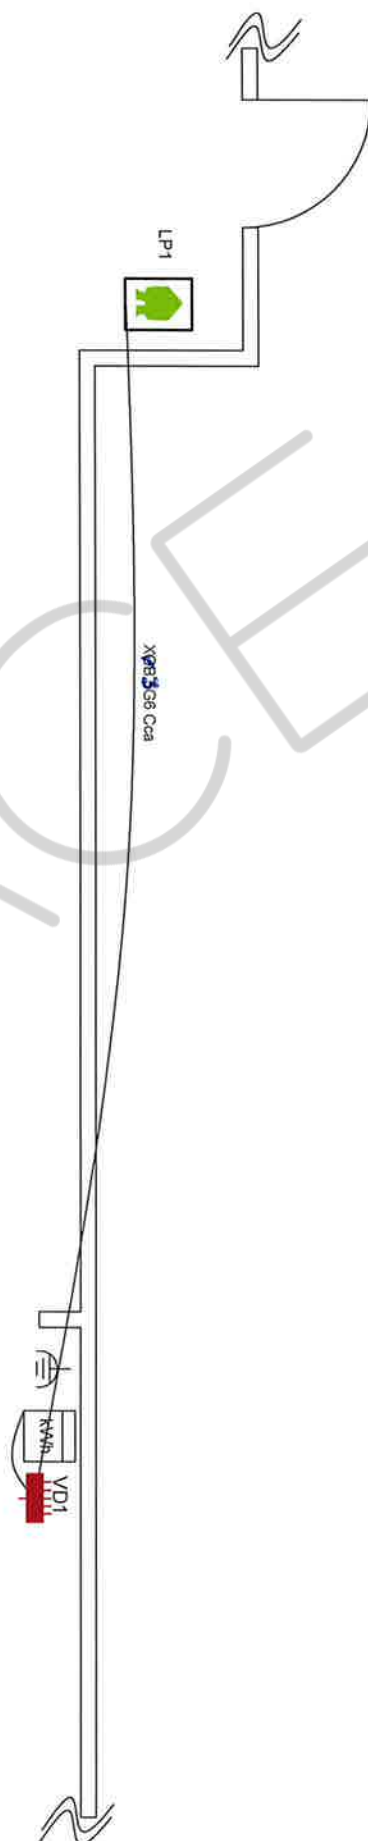

Eendraadschema

Projectnaam: Vercruyse Wouter

Net:

TT

Corr:

Tek:

BD

Datum:

25/02/2025

Locatie:
Izegem

Blad: 1

Van: 3

Schaal: 1:20

Brahim Ichamrach
ACEG VZW N305

Projectnaam:	Vercruysse Wouter	Net:		TT	Rev.:	Tek.:	BD
Datum:	25/02/2025						
				Locatie:	Izegem	Blad:	Van
						3	3

Schaal: 1:1

